



REPUBLIKA E KOSOVËS / REPUBLIKA KOSOVA / REPUBLIC OF KOSOVO

QEVERIA E KOSOVËS / VLADA KOSOVA / GOVERNMENT OF KOSOVA

MINISTRIA E EKONOMISË DHE AMBIENTIT / MINISTARSTVO EKONOMIJE I ŽIVOTNE SREDINE / MINISTRY OF ECONOMY AND ENVIRONMENT

AGJENCIA KADASTRALE E KOSOVËS / KATASTARSKA AGENCIJA KOSOVA / KOSOVA CADASTRAL AGENCY


## Raport i njësisë kadastrale

Zonë kadastrale: Muhoc

Lloji i njësisë kadastrale: Parcelë

Nr i njësisë kadastrale: P-72217061-00045-0

Siper.grafike 17910m<sup>2</sup>

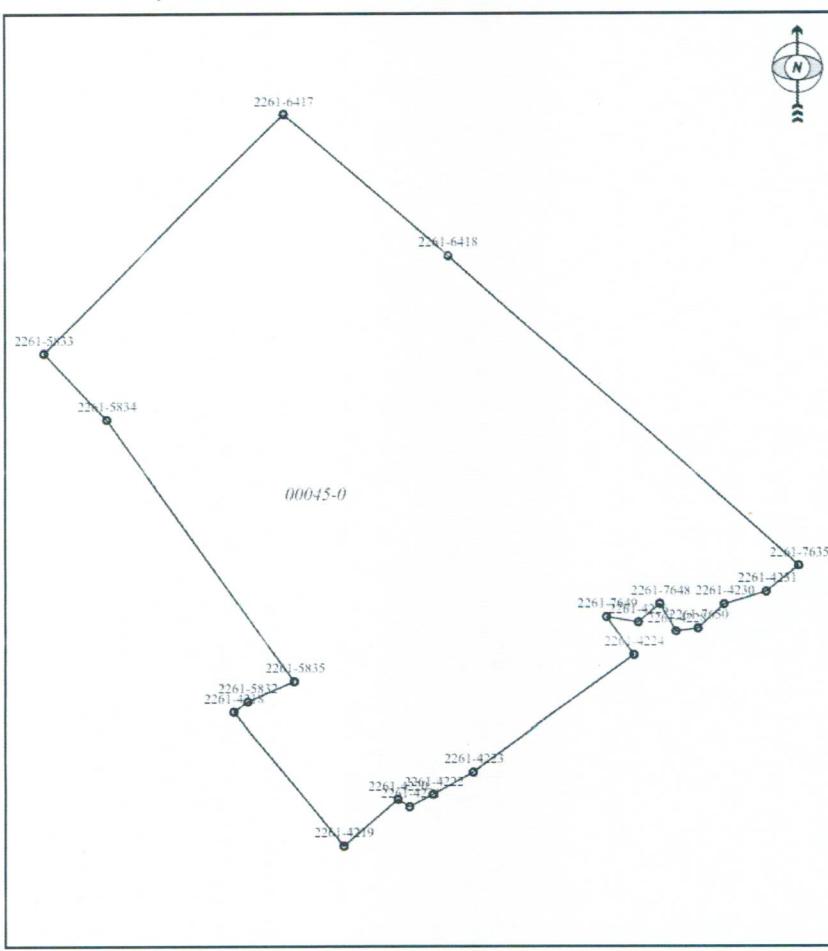

Pika	Y	X
2261-5832	7512505.186	4695653.752
2261-5835	7512517.306	4695659.112
2261-5834	7512468.208	4695728.093
2261-5833	7512451.591	4695745.815
2261-6417	7512514.715	4695808.834
2261-6418	7512557.812	4695771.423
2261-7635	7512649.582	4695689.616
2261-4231	7512640.968	4695682.714
2261-4230	7512629.907	4695679.455
2261-7650	7512623.028	4695673.094
2261-4228	7512617.227	4695672.296
2261-7648	7512612.976	4695679.590
2261-4226	7512607.307	4695674.746
2261-7649	7512599.032	4695676.118
2261-4224	7512606.167	4695666.116
2261-4223	7512564.266	4695635.270
2261-4222	7512553.725	4695629.420
2261-4221	7512547.545	4695626.171
2261-4220	7512544.455	4695628.121
2261-4219	7512530.315	4695615.922
2261-4218	7512501.516	4695651.073

Scale: 1:1815

Proseset paraprake:

Krijuar nga

Pozita:

Emri: Enver

Mbiemri: Pajaziti

Emri i shfrytëzuesit(kodi): Enver.Pajaziti

Data: 12.10.2020

Koha: 09:01:40

Nenshkrimi:





Numri i Protokollit

224/2020

Republika e Kosovës  
Republika Kosova-Republic of Kosova  
Qeveria -Vlada-Government

Ministria e Mjedisit dhe Planifikimit Hapësinor /Ministarstvo Sredine i Prostornog Planiranja/Ministry of Environment and Spatial Planning

AGJENCIA KADASTRALE E KOSOVËS/ KATASTARSKA AGECAJA KOSOVA/ KOSOVA CADASTRAL AGENCYFormulari nr. 5**KËRKESË PËR SHERBIMET KADASTRALE NGA GJEODETI APO KOMPANIA GJEODETE E LICENCUAR**

Gjeodeti Kompania gjeodete e licencuar: Sead Prushi	Numri i licencës: 152
---	-----------------------

Komuna: Ferizaj	Zona Kadsatrale: Muhoc
-----------------	------------------------

Numri i njësisë kadastrale: 45-0
----------------------------------

**1. Të dhënrat për parashtruesin e kërkesës**

Emri / Emri i Kompanisë: Sabedin	Mbiemri: Marevci	Emri i prindit: Hamdi
Numri personal: 1003254263	Adresa: Ferizaj	
Numri i biznesit: (për person juridik dhe kompani)		Nr. Tel: +383 049/498-597

**2. Parashtruesi i kërkesës:  Pronar -  Shfrytëzues -  Përfaqësues i Autorizuar****3. Lista e dokumenteve të nevojshme:**

Pronari/Shfrytëzuesi	Përfaqësues i Autorizuar
1 <input checked="" type="checkbox"/> Letërnjoftimin / Certifikatë biznesi (kopje)	1 <input type="checkbox"/> Letërnjoftimin / Certifikatë biznesi (kopje)
2 <input checked="" type="checkbox"/> Vërtetimi i tatimit në pronë	2 <input type="checkbox"/> Vërtetimi i tatimit në pronë
3 <input checked="" type="checkbox"/> Çertifikata e pronës	3 <input type="checkbox"/> Çertifikata e pronës
4 <input checked="" type="checkbox"/> Kopja e planit	4 <input type="checkbox"/> Kopja e planit

**4. Kërkesa për:**

1 <input type="checkbox"/> Ndërrim të kulturës së parcelës	6 <input type="checkbox"/> Matjen dhe regjistrimin e ndërtesës
2 <input checked="" type="checkbox"/> Ndarjen e parcelës	7 <input type="checkbox"/> Matjen dhe regjistrimin e pjesës së ndërtesës
3 <input type="checkbox"/> Bashkimin e parcelës	8 <input type="checkbox"/> Punë të veçanta gjeodezike
4 <input type="checkbox"/> Përcaktimin e kufijve të parcelës	9 <input type="checkbox"/> Matja e ndërtesës për legalizim
5 <input type="checkbox"/> Ri-regullimin e kufirit të parcelës	10 <input type="checkbox"/> Riregjistrim i pjesës grafiqe

Data: 05.10.2020

Nënshkrimi: \_\_\_\_\_





REPUBLIKA E KOSOVËS - REPUBLIKA KOSOVA - REPUBLIC OF KOSOVA

KOMUNA FERIZAJ - OPŠTINA UROŠEVAC - MUNICIPALITY OF FERIZAJ



### DEFTESE-PRIZNANICA

NF/FN/NB600629804

Nr. Serik/ Ser Br./ Ser No  
**081239**

**1174040954**

Numri Personal / Licni Broj

**Sead Prushi**

Pagoi / Isplatio

Lloji i Pageses / Splacajna

**Kërkes për blerjen e produkteve kadastrale**

Pershkrimi / Opis

**10.00**

Shuma / Iznos

**10-942/05-0085900/20**

Numri i Protokolit / Broj Protokola

**09/10/2020**

Data / Datum



**Lebibe.Sadiku**

Arketari / Blagojnike

Nenshkrimi / Potpis

**Vlera për pagesë: 10.00**

**Numri i tel. fiks**

**Numri i tel. mobil**

**049/535-250**

**Statusi i lëndës**

**Ne proces**

**2. Mënyra e pranimit**

**Kërkesa**

**3. Ju lutemi të shkruani kërkesën apo ankesën tuaj në detaje:**

Kërkes për blerjen e produkteve kadastrale pika detale 45-0 Zk Muhoc.

#### 4. Dokumentet e bashkangjitura:

Nr. Lloji i dokumentit

#### 5. Dëshmia e aplikuesit për vërtetësi

Unë **Sead Prushi** vërtetoj se informatat e lartshënuara janë të vërteta.

\*Ju lutemi të kërkoni nga zyrtari/ja fletëdëshminë për dorëzimin e kësaj kërkeze dhe dokumenteve të bashkangjitura

(Nenshkrimi)



REPUBLIKA E KOSOVËS - REPUBLIKA KOSOVA - REPUBLIC OF KOSOVA

KOMUNA FERIZAJ - OPŠTINA UROŠEVAC - MUNICIPALITY OF FERIZAJ



### DEFTESE-PRIZNANICA

NF/FN/NB600629804

**1174040954**

Numri Personal / Licni Broj

**Sead Prushi**

Pagoi / Isplatio

Lloji i Pageses / Splacajna

**Kërkes për blerjen e produkteve kadastrale**

Pershkrimi / Opis

**10.00**

Shuma / Iznos

**10-942/05-0086388/20**

Numri i Protokolit / Broj Protokola

**12/10/2020**

Data / Datum

**Zymer.Bega**

Arketari / Blagojnike

Nenshkrimi / Potpis





Matje Gjodezike  
Shërbime Kadastrale  
Projektimi Inxhinierike  
Tel: +383 (0) 49-535-250  
liridonsejdiu88@gmail.com

## N.SH. "Geo Coding"

Faturë

Nr: 59/2020

Shitësi:

N.SH. "Goe Coding"

Blerësi: *Sabedin (Hamdi) Marevci*

Pronari:

LIRIDON SEJDIU

1003254263

NRB:

811384528

NRB:

### *Numri Fiskal:*

811384528

Nr. Fiskal:

Adresa:

Rr. "12 Qershori" - Ferizaj

*Adresa:*

II/Bankare

130400100278326000.00%

LL/Bankare

Data: 14.10.2020

Pagesa: *Cash*

Komenti: 1. BPB 13-04-0010027832.69  
2. Banka Ekonomike 1304001002783269

Pranović



### *Dorëzoi:*

102



**Republika e Kosovës**

*Republika Kosova - Republic of Kosovo*

Qeveria e Kosovës - Vlada Kosova - Government of Kosovo

Ministria e Infrastrukturës dhe Ambientit/ Ministrastvo Infrastrukture i Sredine/ Ministry of Infrastructure and Environment

AGJENCIA KADASTRALE E KOSOVËS/ KOSOVSKA KATASTARSKA AGENCIJA/ KOSOVA CADASTRAL AGENCY

## MBËSHTJELLËS I LËNDËS

Gjeodeti / Kompania gjeodete e licencuar: **SEAD PRUSHI**

Numri i licencës: **152**

Numri i Protokollit: **224/2020**

LËNDA:

1.  Ndërrim të kulturës së parcelës
2.  Ndarjen e parcelës
3.  Bashkimin e parcelës
4.  Përcaktimin e kufijve të parcelës
5.  Ri-rregullimin e kufirit të parcelës
6.  Matjen dhe regjistrimin e ndërtesës
7.  Matjen dhe regjistrimin e pjesës së ndërtesës
8.  Regjistrimi i servitutit
9.  Punë të veçanta gjeodezike
10.  Matja e ndërtesës për legalizim

“GJEODET I LICENCUAR”

+383 44 791 828

e-mail: progeo2017@gmail.com

Data: **13/10/2020**

Vendi: **FERIZAJ**

.....

(Nënshkrimi dhe vula)

## Përbajtja:

1.  Kërkesa e palës
  2.  Dëshmia e burimit të të dhënave zyrtare
  3.  Dëshmia e pagesës për të dhënat e pranuara
  4.  Fatura apo kuponi fiskal e lëshuar shërbimet kadastrale sipas UA 11/2019 dhe 12/2019
  5.  Procesverbali nga terreni
  6.  Manuali i njësive kadastrale
  7.  Regjistri i ndërrimeve
  8.  Lista e koordinatave të matura
  9.  Formulari i korrigjimit të sipërfaqes
  10.  Leternjoftimi i pronarit
  11.  Certifikatën e pronësisë
  12.  Leternjoftimi kopje i parashtruesit të kërkesës
  13.  Leternjoftimi kopje i fqinjëve
  14.  Dokumentacioni i gjeodetit të licencuar

## Dokumente tjerar:



Дата издавања: Date of issue  
02.08.2018  
Локација: Место издавања: Location  
MPB / MUP / MIA  
№. Personal: Personal No  
1003254263  
Ид. кард. №.: ID Card No.  
ID1035316  
Локација: Место издавања: Location  
MUHOC. FERIZAJ

IDRKSID10353160<<<<<<<<<<<  
5407316M2808026RKS1003254263<6  
MAREVCI<< SABEDIN <<<<<<<<<



Republika e Kosovës / Republika Kosova / Republic of  
Komuna e FERIZAJ / Opština UROŠEVAC / Municipality



Bazuar në nenin 18 të ligjit 03/L-204 për tatimin në pronë, si dhe udhëzimit administrativ nr. 7/2011 të lëshuar nga MF, i cili ka të bëjë me urdhëresat e ndalimit të shërbimeve komunale për detyrim të pagesës së tatimit në

Na osnovu člana 18, zakona 03/L-204 za poreza na imovinu i administrative uredbe MF br. 7/2011, u vezi zabrane opštinskih usluga za prinudu uplate poreza na imovinu, izdaje se ova:

Based on the article 18 of LAW 03/L-204 on property tax and administrative instruction MF no. 7/2011 on termination of services for enforcement of the municipal property tax, the municipal Property Tax Office

Nr / Br / No

22514195

09/10/2020

## VËRTETIM POTVRDA CERTIFICATE

Me të cilin vërtetohet se tatimpaguesi  
Kojim se potvrđuje da je poreznik  
that certifies that taxpayer

SABEDIN MAREVCI

FERIZAJ

Komuna / Opština / Municipality

FERIZAJ

adresa / adresa / address

I ka kryer pjesërisht / plotësisht obligimet e tatimit në pronë  
Delimično/ izveršio uplatu poreskih obaveza  
has partially / fulfilled obligations on property tax

SABEDIN HAMDI MAREVCI

Vërtetimi lëshohet në bazë të kërkesës së / Potvrda se izdaje na zahtev / Certificate is issued by

Për nevoja personale  
dhe shërben për / i služi za / and is used for

Shënime shtesë / Druge podatke / Additional info





**Republika e Kosovës**

**Republika Kosova-Republic of Kosovo**

*Qeveria - Vlada - Government*

**MINISTRIA E EKONOMISË DHE AMBIENTIT / MINISTARSTVO EKONOMIJE I ŽIVOTNE SREDINE / MINISTRY OF ECONOMY AND ENVIRONMENT  
AGJENCIA KADASTRALE E KOSOVËS / KATASTARSKA AGENCIJA KOSOVA / KOSOVO CADASTRAL AGENCY**

## **CERTIFIKATË / CERTIFIKAT / CERTIFICATE**

**NJËSIA KADASTRALE / KATASTARSKA JEDINICA / CADASTRAL UNIT : P-72217061-00045-0**

Numri i lëndës / Broj Predmet / Case Referent Number:	Certificate draft
Data dhe koha e lëshimit / Datum i vreme izdavanja / Date and time of submission:	13.10.2020 - 13:03
Komuna / Opština / Municipality:	Ferizaj / Uroševac / Ferizaj
Zona kadastrale / Katastarska Zona / Cadastral Zone:	MUHOC / MUHOVCE / MUHOFC
Zyra Kadastrale Komunale / Opštinska Katastarska Kancelarija / Municipal Cadastral Office:	Ferizaj / Uroševac / Ferizaj

### **A. TË DHËNAT PËR NJËSİNË KADASTRALE / PODACI O KATASTARSKOJ JEDINICI / CADASTRAL UNIT DATA**

Numri i njësisë kadastrale Broj katastarske jedinice Cad. Unit. No.	Lloji i njësisë Vrsta Jedinice Unit Type	Lloji i pronës Vrsta imovine Property Type	Zona U/R G/S U/R	Sipërfaqja Površina Area (m <sup>2</sup> )	Përshkrim Opis Description	Krijuar më datën Uradjeno na dan Created On	Azhuruar Ažurirano Updated
P-72217061-00045-0	PARCELË / PARCELA / PARCEL	Pronë private / Privatna Imovina / Privately owned Land		17857			

### **A.1 ADRESA E NJËSISË KADASTRALE / ADRESA KATASTARSKE JEDINICE /CADASTRAL UNIT ADDRESS**

Vendbanimi - adresa Prebivaliste - adresa Resident - address	Kodi Postal Poštanski Kod Postal Code	Hollësitë e adresës Pojedinosti adrese Address Details	Krijuar më datën Uradjeno na dan Created On	Azhuruar Ažurirano Updated
BREGU PRELEZ/BREGU PRELEZ/BREGU PRELEZ		BREGU PRELEZ		

## 2.2 LLOJI I SHFRYTËZIMIT / VRSTA KORISCENJA / TYPE OF USE


Numri Broj Number	Lloji i shfrytëzimit të parcelës Vrsta koriscenja parcele Parcel Type Of Use	Shfrytëzimi aktual i parcelës Trenutno koriscenje parcele Parcel Current Use	Kualiteti i klasës Kvalitet klase Quality Class	Sipërfaqja (m <sup>2</sup> ) Površina (m <sup>2</sup> ) Area (m <sup>2</sup> )
1	Bujqësore/Poljoprivredno/Agriculture	Arat/Njive/Arable	Arë E Klasës 4/Njiva 4 Klase/4th Class Arable Land	17857

## PRONARI/POSEDUESI - VLASNIK/DRŽALAC - OWNER/POSSESSOR

Të drejtat Prava Rights	Emri Ime Name	Nr. personal Licni broj ID. No.	Vendbanimi Prebivaliste Resident	Kodi postal Poštanski kod Postal code	Hollësitë e adresës Pojedinosti adrese Address details	Pjesa e pronës Deo imovine Share quota	Pershkrimi Opis Description	Azhuruar Ažurirano Updated
Ekë Posedim / Državina / co-possessor	<b>BISLIMI NAIM</b>	1011550874	MUHOC / MUHOVCE / MUHOFC /			1/8	15/2018- Kontratë për dhurimin e paluajtshmërisë LRP.nr.10103/2018, Nr.ref.3422/2018	03.09.2018
Ekë Posedim / Državina / co-possessor	<b>BISLIMI AVDUSH (BISLIM)</b>	KCID2209565	MUHOVC / MUHOVC / MUHOVC /			2/8		03.09.2018
Ekë Posedim / Državina / co-possessor	<b>BISLIMI EMRUSH (BISLIM)</b>	KCID2209567	MUHOVC / MUHOVC / MUHOVC /			2/8		03.09.2018
Ekë Posedim / Državina / co-possessor	<b>MAREVCI SABEDIN (HAMDI)</b>	1003254263	MUHOC / MUHOVCE / MUHOFC /			1/8	4/2014	03.09.2018
Ekë Posedim / Državina / co-possessor	<b>BISLIMI ESAT (BEQIR)</b>	2011069137	MUHOC / MUHOVCE / MUHOFC /			2/8	21/2013	03.09.2018





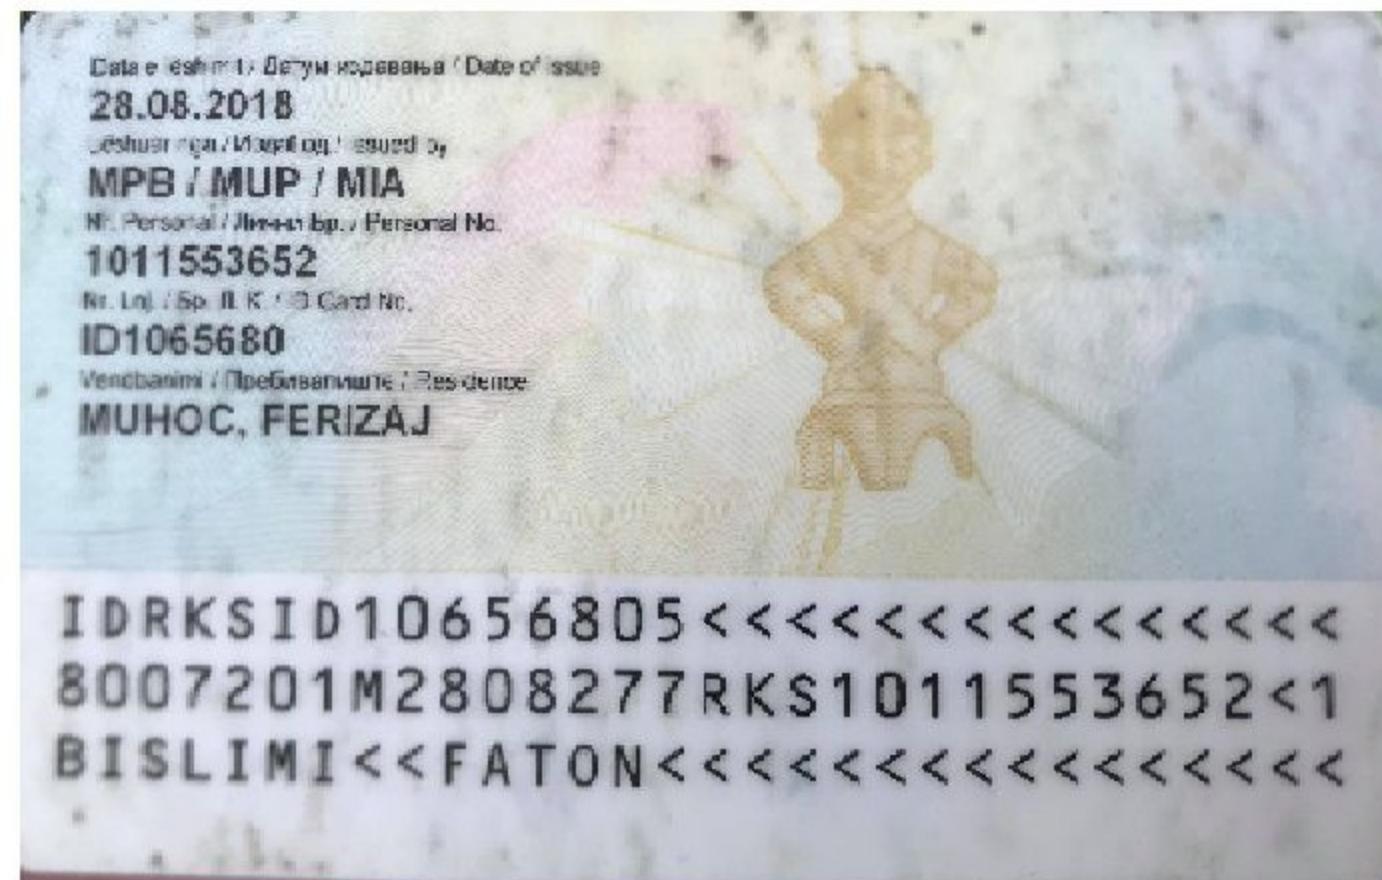









# Republika e Kosovës

Republika Kosova-Republic of Kosovo

Qeveria e Kosovës- Vlada Kosova- Government of Kosovo

Ministria e Infrastrukturës dhe Ambientit/ Ministrastvo Infrastrukture i Sredine/ Ministry of Infrastructure and Environment

AGJENCIA KADASTRALE E KOSOVËS/KOSOVSKA KATASTARSKA AGENCIJA/ KOSOVO CADASTRAL AGENCY

## PROCESVERBALI NGA TERRENI

Gjeodeti / Kompania gjeodete e licencuar: <b>SEAD PRUSHI</b>	Numri i licencës: <b>152</b>
--	------------------------------

Komuna: <b>FERIZAJ</b>	Zona Kadastrale: <b>MUHOC</b>
------------------------	-------------------------------

Numri i njësisë kadastrale: <b>00045-0</b>
--

Matja/piketimi është realizuar me:	
GPS/GNSS	<input checked="" type="checkbox"/>
Stacion Total	<input type="checkbox"/>

### 1. Përshkimi i procesit:

**ME KËRKES TË PRONARIT FAKTIK Z. SABEDIN MAREVCI, SOT ME DATË 08.10.2020 KEMI BËRË MATJEN PËR PJESEN E PARCELËS 45-O SIPAS GJENDOJES FAKTIKE NË PRANI TË HEGJANIKËVE TË POSHTËNËNSHKRUAR. MATJA ËSHTË BËRË SIPAS PREZENTIMIT TË TË GJITHË MEYHANIKËVE.**

### 2. Vërejtje:

### 3. Nënshkrimi i palëve

Pronarët janë pajtuar me pikat definitive kufitare të vendosura në terren nga të cilat derivohet sipërfaqja definitive që do të regjistrohet në Sistemin e Informacioneve Kadastrale për Tokën në Kosovë.

Të poshtëshënuarve u lexohet procesverbalı dhe janë pajtuar me anë të nënshkrimit më poshtë.

Emri (emri i prindit) mbiemri	Numri personal	Numri i njësisë kadastrale	Nënshkrimi
HILAIM BISLIMI	2018181277		<i>Bislimi</i>
PËRPARIM BISLIMI	1172960673		<i>Bislimi</i>
SHUKRI BISLIMI	1018181262	00045-0	<i>Shukri</i>
ARMEND MAREVCI	1233302143		<i>Armend</i>
KUJTIM BISLIMI	1172960410		<i>Kuvtim</i>
FATON BISLIMI	1011553652		<i>Faton</i>
SABEDIN MAREVCI	1003294263		<i>Sabedin</i>

Nënshkrimi dhe vula e gjodetit: *Bislimi*

Data: 08.10.2020





**Republika e Kosovës**  
**Republika Kosova-Republic of Kosova**  
**Qeveria - Vlada-Government**  
**Ministria e Mjedisit dhe Planifikimit Hapësinor /Ministarstvo Sredine i Prostornog Planiranja/Ministry of Environment and Spatial Planning**  
**AGJENCIJA KADASTRALE E KOSOVËS / KATASTARSKA AGECIJA KOSOVA/ KOSOVA CADASTRAL AGENCY**

Zyra kadastrale komunale / Opštinska katastarska kancelarija: Ferizaj

45-0

Zona kadastrale / Katastarska zona: Muhoc


Nr. i njësisë kadastrale / Br. katastarske jedinice : \_\_\_\_\_  
 Numri i lëndës / Broj predmeta: \_\_\_\_\_

Lloji i njësisë kadastrale / Vrsta katastarske jedinice : Parcelë

Shkalla e zvoglimit / Razmera plana : 1:2000



Legjenda	
Parcela bazë	
Parcela fqinje	
Parcela e re	
Nr parc bazë	45-0
Nr parc fqinje	43-0
Nr parc të re	45-1
Pikë e ndarjes	2
Pikë e kufirit	5833
Pikë e rreugllimit	4

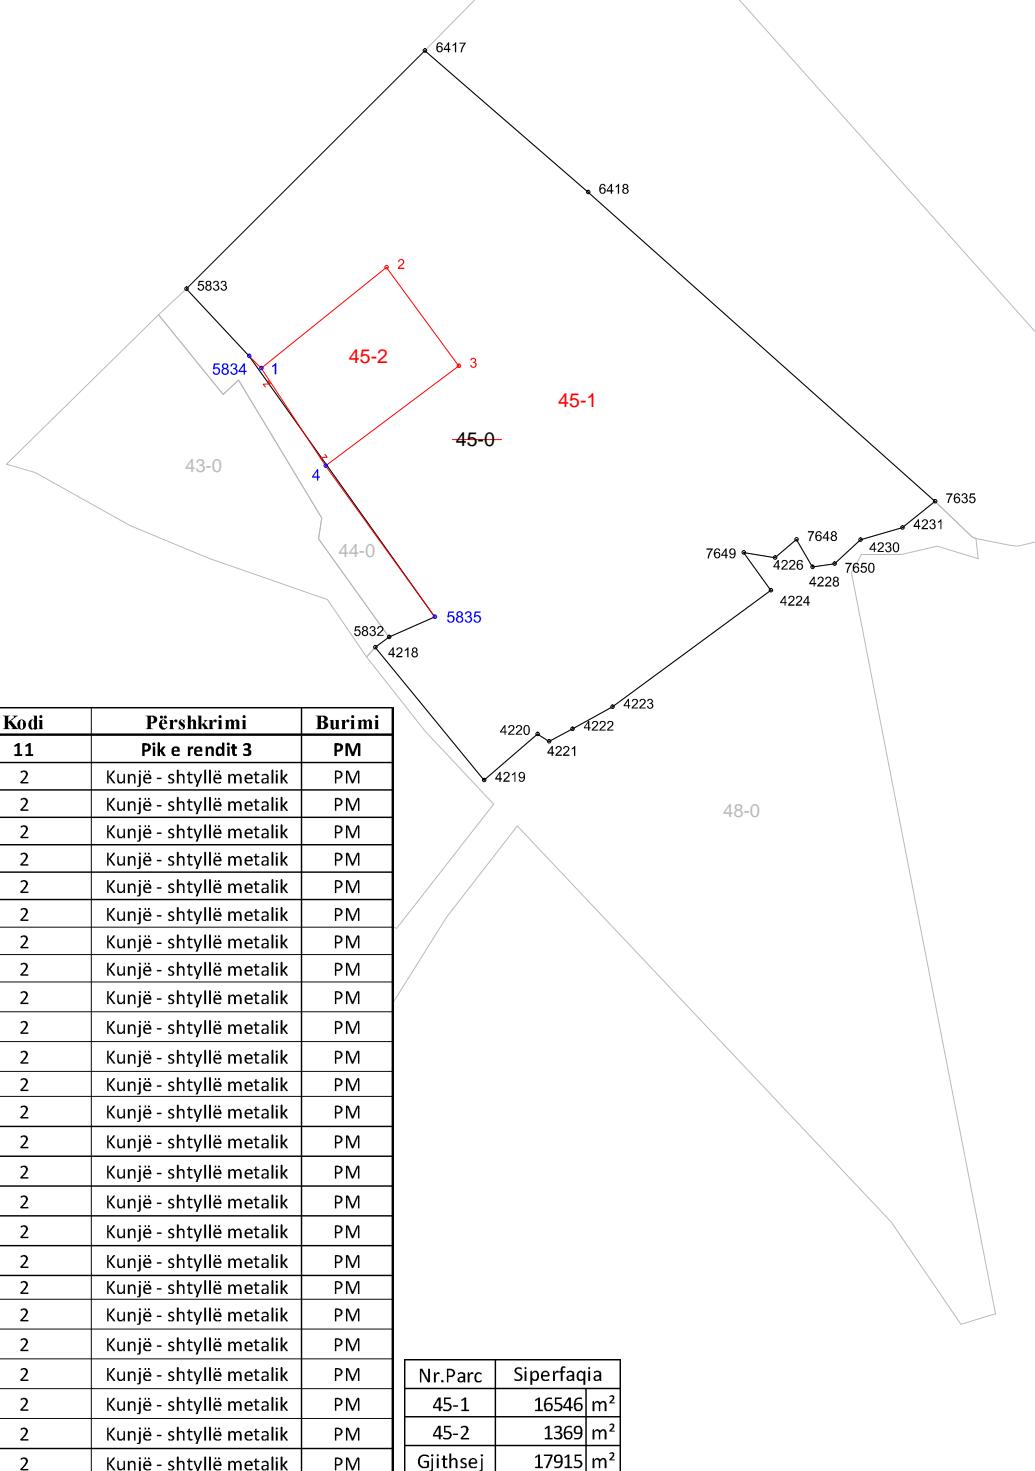

Rilevoi / Snimio: SEAD PRUSHI  
 (emri dhe mbiemi i gjeddetit/kompanisë/ ime i prezime geodeta/ kompanije)

Nr. i licencës / Br. licence: 152

V.V.

Nënshkrimi / Potpis:

Aprovoi / Usvojio: \_\_\_\_\_  
 (emri dhe mbiemi i pësonit zyrtar/ ime i prezime sluzbenog lica)

Data e rilevimit / Datum snimanja: 08.10.2020

Data e aprovimit / Datum usvajanja: \_\_\_\_\_



## Open Documents

Point Id	/	Point Class	Date/Time	Easting	Northing	Ellip. Hgt.	Code	Posn. + Hgt. Qlty
✓ 1		Measured	10/08/2020 14:58:29	7512502.6957	4695754.0297	618.7805	MEXH	0.0136
✓ 2		Measured	10/08/2020 14:59:13	7512502.5106	4695753.9194	618.7677	KABLLA RRYMES	0.0121
✓ 3		Measured	10/08/2020 15:01:04	7512504.5497	4695751.5512	619.3179	MEXH	0.0493
✓ 4		Measured	10/08/2020 15:04:19	7512515.2185	4695736.8492	619.3506	MEXH	0.0463
✓ 5		Measured	10/08/2020 15:07:36	7512523.6850	4695725.4321	618.8262	MEXH	0.0194
✓ 6		Measured	10/08/2020 15:13:47	7512473.3937	4695726.4229	619.0257	MEXH	0.0205
✓ 7		Measured	10/08/2020 15:15:31	7512471.3299	4695724.8840	619.0217	MEXH	0.0219
✓ 8		Measured	10/08/2020 15:16:20	7512492.5595	4695692.7222	618.9345	MEXH	0.0236
✓ 9		Measured	10/08/2020 15:17:20	7512490.6499	4695700.6563	618.9570	MEXH	0.0151
✓ 220086PM		Measured	10/08/2020 17:10:57	7512362.3835	4694374.6410	620.6741		0.0235
✓ A4		Measured	10/08/2020 15:18:33	7512488.4162	4695698.9796	618.9570		0.0332
✓ A4218		Measured	10/08/2020 15:52:11	7512501.5087	4695651.0672	618.8260		0.0322
✓ A4219		Measured	10/08/2020 15:50:09	7512530.3158	4695615.9212	618.7437		0.0294
✓ A4220		Measured	10/08/2020 15:50:00	7512544.4617	4695628.1283	618.5720		0.0286
✓ A4221		Measured	10/08/2020 15:48:54	7512547.5382	4695626.1783	618.5450		0.0263
✓ A4222		Measured	10/08/2020 15:48:48	7512553.7197	4695629.4133	618.4780		0.0335
✓ A4223		Measured	10/08/2020 15:45:40	7512564.2727	4695635.2618	618.3750		0.0319
✓ A4226		Measured	10/08/2020 15:40:56	7512607.3005	4695674.7397	617.8240		0.0304
✓ A4228		Measured	10/08/2020 15:35:38	7512617.2182	4695672.2879	617.7420		0.0290
✓ A4230		Measured	10/08/2020 15:33:18	7512629.9017	4695679.4479	617.5990		0.0281
✓ A4231		Measured	10/08/2020 15:32:11	7512640.9744	4695682.7057	617.4850		0.0336
✓ A5832		Measured	10/08/2020 15:52:21	7512505.1910	4695653.7458	618.8390		0.0277
✓ A5833		Measured	10/08/2020 15:21:14	7512451.5972	4695745.8077	619.0882		0.0295
✓ A5834		Measured	10/08/2020 15:20:59	7512468.1997	4695728.0857	619.0333		0.0270
✓ A5835		Measured	10/08/2020 15:52:29	7512517.3122	4695659.1047	618.8456		0.0266
✓ A6417		Measured	10/08/2020 15:25:37	7512514.7223	4695808.8277	618.8073		0.0290
✓ A6418		Measured	10/08/2020 15:27:48	7512557.8173	4695771.4292	618.2345		0.0269
✓ A7635		Measured	10/08/2020 15:30:02	7512649.5747	4695689.6107	617.3845		0.0277
✓ A7648		Measured	10/08/2020 15:38:46	7512612.9823	4695679.5812	617.7690		0.0269
✓ A7649		Measured	10/08/2020 15:43:14	7512599.0397	4695676.1253	617.8430		0.0277
✓ A7650		Measured	10/08/2020 15:34:29	7512623.0332	4695673.0885	617.6960		0.0277
✓ B5833		Measured	10/08/2020 16:30:35	7512451.6025	4695745.8139	619.1002		0.0332
✓ B5834		Measured	10/08/2020 16:33:42	7512468.1924	4695728.0804	619.0236		0.0294
✓ B5835		Measured	10/08/2020 16:39:49	7512517.3185	4695659.0959	618.8656		0.0265
✓ RTCM-Ref 0003	Reference		10/08/2020 14:33:09	7503168.9298	4699391.6087	628.0260		0.0000
✓ RTCM-Ref 2893	Reference		10/08/2020 15:15:12	7512506.9598	4695753.7969	614.5589		0.0000



Republika e Kosovës

Republika Kosova - Republic of Kosovo

Qeveria e Kosovës - Vlada Kosova - Government of Kosovo

Ministria e Infrastrukturës dhe Ambientit/ Ministrastvo Infrastrukture i Sredine/ Ministry of Infrastructure and Environment  
AGJENCIA KADASTRALE E KOSOVËS/ KOSOVSKA KATASTARSKA AGENCIJA/ KOSOVA CADASTRAL AGENCY

GJENDJA E VJETËR / STARO STANJE									GJENDJA E RE / NOVO STANJE					
Numri rendor, Redni broj	Komuna Opština	Zona kadastrale Katastarska zona	Mbiemri, Emri (Emri i Babës) Adresa e vendbanimit  Prezime, Ime (Ime Oca) Adresa prebivalista  1. Pronar - Vlasnik - Owner 2. Posedues - Posednik - Possessor 3. Shfrytëzues - Korisnik - User	Nr. personal nga: Personalni Br. iz:  1. Regj. i qytetarëve Registar gradana  2. Regj. i bizneseve Registar biznisa	Nr. i Njësisë Br. Jedinice  1. (P) Parcela u/r 2. (O) Ndërtesa u/r Zgrada  3. (O) Pj. e ndërt. u/r Deo Zgrade	Kultura, klasa Shfrytëzimi aktual  Aktuelna upotreba	□ □ □ Sipërfaqja, Površina (m²)	Përshkrimi i gjendjes së Njësisë Opis stanja Jedinice  1. Adresa, Vendi i quajtur Adresa, Zvano mesto  2. Infrastruktura Infrastruktura  3. Tjera karakterist.(referen ca) Ostale karakterist.(referen sa)	Mbiemri, Emri (Emri i Babës) Adresa e vendbanimit  Prezime, Ime (Ime Oca) Adresa prebivalista  1. Pronar - Vlasnik 2. Posedues - Posednik 3. Shfrytëzues - Korisnik	Nr. i Njësisë Br. Jedinice  1. (P) Parcela u/r 2. (O) Ndërtesa u/r Zgrada  3. (O) Pj. e ndërt. u/r Deo Zgrade	Kultura, klasa Shfrytëzimi aktual  Aktuelna upotreba	□ □ □ Sipërfaqja, Površina (m²)	Dokumenti në të cilin bazohet ndërrimi dhe rezultati i shiqimit në vend të ngjarjes nga personi zytar për mirëmbajjen e kadastrit.	
1	2	3	4	5	6	7	8	9	10	11	12	13	14	
1	Ferizaj	Muhoc	1/8 Naimi Bislimi 2/8 Avdush (Bislim) Bislimi 2/8 Emrush (Bislim) Bislimi 1/8 Sabedin (Hamdi) Marevci 1/8 Esat (Beqir) Bislimi	1003254263 KCID2209565 1 KCID2209567 1003254263 2011069137	1 00045-0 R	Arë (4)	17915	Bregu Prelez	1/8 Naimi Bislimi 2/8 Avdush (Bislim) Bislimi 2/8 Emrush (Bislim) Bislimi 1/8 Sabedin (Hamdi) Marevci 1/8 Esat (Beqir) Bislimi	00045-1 2/8 Avdush (Bislim) Bislimi 2/8 Emrush (Bislim) Bislimi 1/8 Sabedin (Hamdi) Marevci 1/8 Esat (Beqir) Bislimi	Arë (4)	16546		
										1	R	00045-2	Arë (4)	1369
												Gjithësej		17915
Gjeodeti/kompania e licencuar: SEAD PRUSHI				Nr i licencës: 152					Nënshkrimi dhe vula:					



Republika e Kosovës  
Republika Kosova-Republic of Kosovo  
Qeveria e Kosovës- Vlada Kosova- Government of Kosovo  
Ministria e Infrastrukturës dhe Ambientit/ Ministarstvo Infrastrukture i Sredine/ Ministry of Infrastructure and Environment  
AGJENCIA KADASTRALE E KOSOVËS/KOSOVSKA KATASTARSKA AGENCIJA/ KOSOVO CADASTRAL AGENCY

<b>Komuna: Ferizaj</b>	<b>Zona Kadastrale: Muhoc</b>
<b>Numri i njësis kadastrale: 00045-0</b>	<b>Sistemi koordinat: Kosova Ref01</b>

Nr	Y	X	H	Kodi	Përshkrimi	Burimi
<b>220086PM</b>	<b>7512362.384</b>	<b>4694374.641</b>	<b>620.674</b>	<b>11</b>	<b>Pik e rendit 3</b>	<b>PM</b>
4218	7512501.516	4695651.073	618.826	2	Kunjë - shtyllë metalik	PM
4219	7512530.315	4695615.922	618.744	2	Kunjë - shtyllë metalik	PM
4220	7512544.455	4695628.121	618.572	2	Kunjë - shtyllë metalik	PM
4221	7512547.545	4695626.171	618.545	2	Kunjë - shtyllë metalik	PM
4222	7512553.725	4695629.420	618.478	2	Kunjë - shtyllë metalik	PM
4223	7512564.266	4695635.270	618.375	2	Kunjë - shtyllë metalik	PM
4224	7512606.167	4695666.116	617.862	2	Kunjë - shtyllë metalik	PM
4226	7512607.307	4695674.746	617.824	2	Kunjë - shtyllë metalik	PM
4228	7512617.227	4695672.296	617.742	2	Kunjë - shtyllë metalik	PM
4230	7512629.907	4695679.455	617.599	2	Kunjë - shtyllë metalik	PM
4231	7512640.968	4695682.714	617.485	2	Kunjë - shtyllë metalik	PM
5832	7512505.186	4695653.752	618.839	2	Kunjë - shtyllë metalik	PM
5833	7512451.591	4695745.815	619.094	2	Kunjë - shtyllë metalik	PM
6417	7512514.715	4695808.834	618.807	2	Kunjë - shtyllë metalik	PM
6418	7512557.812	4695771.423	618.235	2	Kunjë - shtyllë metalik	PM
7635	7512649.582	4695689.616	617.385	2	Kunjë - shtyllë metalik	PM
7648	7512612.976	4695679.590	617.769	2	Kunjë - shtyllë metalik	PM
7649	7512599.032	4695676.118	617.843	2	Kunjë - shtyllë metalik	PM
7650	7512623.028	4695673.094	617.696	2	Kunjë - shtyllë metalik	PM
<b>1</b>	<b>7512471.384</b>	<b>4695724.802</b>	<b>619.022</b>	<b>2</b>	<b>Kunjë - shtyllë metalik</b>	<b>PM</b>
<b>4</b>	<b>7512488.425</b>	<b>4695698.987</b>	<b>618.957</b>	<b>2</b>	<b>Kunjë - shtyllë metalik</b>	<b>PM</b>
<b>5834</b>	<b>7512468.208</b>	<b>4695728.093</b>	<b>619.028</b>	<b>2</b>	<b>Kunjë - shtyllë metalik</b>	<b>PM</b>
<b>5835</b>	<b>7512517.306</b>	<b>4695659.112</b>	<b>618.856</b>	<b>2</b>	<b>Kunjë - shtyllë metalik</b>	<b>PM</b>
<b>2</b>	<b>7512504.528</b>	<b>4695751.534</b>	<b>619.318</b>	<b>2</b>	<b>Kunjë - shtyllë metalik</b>	<b>PM</b>
<b>3</b>	<b>7512523.685</b>	<b>4695725.432</b>	<b>618.826</b>	<b>2</b>	<b>Kunjë - shtyllë metalik</b>	<b>PM</b>

Matja e pikave	Nr. Pikës	Y	X	H	AY	AX	AP
					-0.0053	-0.0062	0.0082
I	5833	7512451.60	4695745.81	619.09			
II	5833	7512451.60	4695745.81	619.10			
I	5834	7512468.2	4695728.086	619.03			
II	5834	7512468.192	4695728.08	619.02			
I	5835	7512517.312	4695659.105	618.85			
II	5835	7512517.319	4695659.096	618.87			

Koordinatat përfundimtare			
Nr	Y	X	H
5833	7512451.600	4695745.811	619.094
5834	7512468.196	4695728.083	619.028
5835	7512517.315	4695659.100	618.856

Gjeodeti / Kompania gjeodete e licencuar:	Sead Prushi	Nënshkrimi dhe vula:
Numri i licencës	152	



**Republika e Kosovës**  
**Republika Kosova-Republic of Kosovo**  
*Qeveria e Kosovës- Vlada Kosova- Government of Kosovo*

Ministria e Infrastrukturës dhe Ambientit/ Ministrastvo Infrastrukture i Sredine/ Ministry of Infrastructure and Environment

**AGJENCIA KADASTRALE E KOSOVËS/KOSOVSKA KATASTARSKA AGENCIJA/ KOSOVO CADASTRAL AGENCY**

**FORMULARI PËR KORIGJIMIN E SIPËRFAQËS**

Gjeodeti / Kompania gjeodete e licencuar: Sead Prushi	Numri i licencës:152
Komuna: Ferizaj	Zona Kadastrale: Muhoc
Numri i njësisë kadastrale: 00045-0	Numri i lëndës: 224/2020

**1. Tabela e ndryshimeve të sipërfaqes**

Numri i parcelës	Sipërfaqja faktike (m <sup>2</sup> )	Sipërfaqja nga SIKTK-T (m <sup>2</sup> )	Ndryshimi (m <sup>2</sup> )	Sipërfaqja e korrigjuar (m <sup>2</sup> )
00045-0	17915	17857	58	17915

Bazuar në procesverbalin e terrenit, pronarët janë pajtuar me pikat definitive kufitare të vendosura në terren nga të cilat edhe është derivuar sipërfaqja definitive që regjistrohet në SIKTK.

Nënshkrimi dhe vula e gjodetit: \_\_\_\_\_

Data: \_\_\_\_\_



**Republika e Kosovës**  
**Republika Kosova-Republic of Kosovo**  
**Qeveria e Kosovës- Vlada Kosova- Government of Kosovo**

Ministria e Infrastrukturës dhe Ambientit/ Ministrastvo Infrastrukture i Sredine/ Ministry of Infrastructure and Environment

**AGJENCIA KADASTRALE E KOSOVËS/KOSOVSKA KATASTARSKA AGENCIJA/ KOSOVO CADASTRAL AGENCY**

**RAPORTI TEKNIK**

Gjeodeti / Kompania gjeodete e licencuar: <b>Sead Prushi</b>	Numri i licencës: <b>152</b>
Komuna: <b>Ferizaj</b>	Zona Kadastrale: <b>Muhoc</b>
Numri i njësisë kadastrale: <b>00045-0</b>	Lloji i lëndës: <b>Ndarje e parcelës</b>

Bazuar në kërkesën e palës **z. Sabedin (Hamdi) Marevci** me numër personal **1003254263** të parashtruar me datën **05/10/2020**, është bërë kërkesa për marrjen e produkteve kadastrale në Zyrën Kadastrale Komunale **Ferizaj** me datë **05/10/2019**.

Pas analizimit të dhënave me datë **08/10/2020** janë realizuar matjet në terren, për (**rilevimin/bashkimin**) e parcelave bazuar në (**gjendjen faktike/sipërfaqe të barazuara**).

Matjet në terren janë realizuar me instrument (GPS Leica 1230), ku fillimisht janë realizuar matjet bazuar në kornizën AKK nr.: 2020/01, pastaj është bërë matja e pikës kontrolluese **220086 (pikë e rendit III)**,

Matje të dyfishta kontrolluese janë realizuar në pikat numër **5833,5834,5835**

*Sfidat gjatë realizimit të matjeve:*

Matje të dyfishta kontrolluese janë realizuar në pikat numër **5833,5834,5835**.

**Raporti në formë tabelare:**

Parcela para ndarjes/bashkimit	Sipërfaqja (m <sup>2</sup> )	Korigjimi i sipërfaqe (po/jo)	Parcela pas ndarjes/bashkimit	Sipërfaqja (m <sup>2</sup> )
00045-0	17915	PO	00045-1	16546 m <sup>2</sup>
			00045-2	1369 m <sup>2</sup>

Nënshkrimi dhe vula e gjodetit: \_\_\_\_\_

Data: \_\_\_\_\_



**Republika e Kosovës**  
**Republika Kosova-Republic of Kosovo**  
*Qeveria - Vlada - Government*

MINISTRIA E EKONOMISË DHE AMBIENTIT / MINISTARSTVO EKONOMIJE I ŽIVOTNE SREDINE / MINISTRY OF ECONOMY AND ENVIRONMENT  
 AGJENCIA KADASTRALE E KOSOVËS / KATASTARSKA AGENCIJA KOSOVA / KOSOVO CADASTRAL AGENCY

**CERTIFIKATË / CERTIFIKAT / CERTIFICATE**

**PERSONI / OSOBA /PERSON : MAREVCI SABEDIN**

Numri i lëndës / Broj Predmet / Case Referent Number:	85910-2020
Data dhe koha e lëshimit / Datum i vreme izdavanja / Date and time of submission:	09.10.2020 - 14:05
Komuna / Opština / Municipality:	Ferizaj / Uroševac / Ferizaj
Zyra Kadastrale Komunale / Opštinska Katastarska Kancelarija / Municipal Cadastral Office:	Ferizaj / Uroševac / Ferizaj

**A. TË DHËNAT PËR PERSONIN / PODACI O OSOBI / PERSON'S DATA**

Mbiemri/Emri i afarizmit (biznesit) Prezime/ Naziv poslovanja (biznisa) Last Name / Business Name	Emri Ime First Name	Emri i babait Ime oca Father's Name	Gjinia Pol Gender	Nr. personal/ biznesit Lični broj/broj poslovanja ID. No.	Shteti i shtetësisë apo regjistrimit Država državljanstva ili uknjiženja Country of citizenship	Ditëlindja/Data e themelimit Rodendan/Dan osnivanja Date of Birth/Establishmen t	Krijuar më datën Uradjeno na dan Created On	Azhuruar Ažurirano Updated
MAREVCI	SABEDIN	HAMDI	Mashkull / Musko / Male	1003254263	KOSOVA / KOSOVA / KOSOVO	31.07.1954	28.02.2014	28.02.2014

**A.1 ADRESA E PERSONIT / ADRESA OSOBE / PERSON'S ADDRESS**

Vendbanimi Prebivaliste Resident	Kodi Postal Poštanski Kod Postal Code	Hollësitë e adresës Pojedinosti adrese Address Details	Adresa tjetër Druga adresa Other address	Azhuruar Ažurirano Updated
MUHOC / MUHOVCE / MUHOFC			MUHOC	



**B. NJESIA KADASTRALE/ KATASTARSKA JEDINICA/CADASTRAL UNIT**

Njësie kadastrale Katastarska jedinica Cadastral unit	Komuna / Opština / Municipality	Zona kadastrale Katastarska zona Cadastral zone	Lloji i njësisë Vrsta jedinice Unit type	Tipi i pronës Tip imovine Property Type /	Kati/ Katet Br.Sprat a/ Spratova Floor number	Vendi i quajtur Zvano mesto Place name	Sipërfaqja Površina Area	Shfrytezimi aktual/Kultura- klasa Aktuelna upotreba/ Kultura-klasa Actual use/Culture-class	Pjesa e pronës Deo imovine Share quota	Lloji i së drejtës Vrsta prava Type of the right	Azhuruar Ažurirano Updated
P-72217061-00043-0	Ferizaj / Uroševac / Ferizaj	MUHOC / MUHOVCE / MUHOF C	PARCELË / PARCELA / parcel	Pronë private Privatna Imovina Privately owned Land /		BREGU PRELEZ / BREGU PRELEZ / BREGU PRELEZ	3246	Tokë Ndërtimore - Oborr - / Buqësore - Kullosat - Kullosë E Klasës 2 / Tokë Ndërtimore - Shtëpi-Ndërtese - / Gradjevinsko zemljiše - Dvoriše - / Poljoprivredno - Pašnjaci - Pasnjak 2 Klase / Gradjevinsko zemljiše - Kuca- Zgrada - / / Construction land - BackYard - / Agriculture - pasture - 2nd Class Pasture / Construction land - House-Building - / /	1 / 8	Bashkë Posedim / SuDrzavina / co-possessor	03.09.2018
P-72217061-00044-0	Ferizaj / Uroševac / Ferizaj	MUHOC / MUHOVCE / MUHOF C	PARCELË / PARCELA / parcel	Pronë private Privatna Imovina Privately owned Land /		BREGU PRELEZ / BREGU PRELEZ / BREGU PRELEZ	1067	Buqësore - Pemishtet - Pemishtë E Klasës 3 / / Poljoprivredno - Vocnjaci - Vocnjak 3 Klase / / Agriculture - orchard - 3rd Class Orchard / /	1 / 8	Bashkë Posedim / SuDrzavina / co-possessor	03.09.2018
P-72217061-00045-0	Ferizaj / Uroševac / Ferizaj	MUHOC / MUHOVCE / MUHOF C	PARCELË / PARCELA / parcel	Pronë private Privatna Imovina Privately owned Land /		BREGU PRELEZ / BREGU PRELEZ / BREGU PRELEZ	17857	Bujqësore - Arat - Arë E Klasës 4 / / Poljoprivredno - Njive - Njiva 4 Klase / / Agriculture - Arable - 4th Class Arable Land / /	1 / 8	Bashkë Posedim / SuDrzavina / co-possessor	03.09.2018

Zyrtari përgjegjës / Odgovorno lice / Official person

Printuar nga / Odštampani od / Printed by: Shpresa.Ramadani | Personi/Osoba/Person: MAREVCI SABEDIN |

P-72217061-00046-0	Ferizaj / Uroševac / Ferizaj	MUHOC / MUHOVCE / MUHOF C	PARCELË / PARCELA / parcel	Pronë private Privatna Imovina Privately owned Land /	BREGU PRELEZ / BREGU PRELEZ / BREGU PRELEZ	17235	Bujqësore - Arat - Arë E Klasës 4 / / Poljoprivredno - Njive - Njiva 4 Klase / / Agriculture - Arable - 4th Class Arable Land / /	1 / 8	Bashkë Posedim / SuDrzavina / co-possessor	03.09.2018
P-72217061-00047-0	Ferizaj / Uroševac / Ferizaj	MUHOC / MUHOVCE / MUHOF C	PARCELË / PARCELA / parcel	Pronë private Privatna Imovina Privately owned Land /	BREGU PRELEZ / BREGU PRELEZ / BREGU PRELEZ	9805	Bujqësore - Arat - Arë E Klasës 4 / / Poljoprivredno - Njive - Njiva 4 Klase / / Agriculture - Arable - 4th Class Arable Land / /	1 / 8	Bashkë Posedim / SuDrzavina / co-possessor	03.09.2018
P-72217061-00048-0	Ferizaj / Uroševac / Ferizaj	MUHOC / MUHOVCE / MUHOF C	PARCELË / PARCELA / parcel	Pronë private Privatna Imovina Privately owned Land /	BREGU PRELEZ / BREGU PRELEZ / BREGU PRELEZ	13461	Bujqësore - Livadhet - Livadh I Klasës 3 / / Poljoprivredno - Poljoprivredno - Livade - Livada 3 Klase / / Agriculture - meadow - 3rd Class Meadow / /	1 / 8	Bashkë Posedim / SuDrzavina / co-possessor	03.09.2018
P-72217061-00049-0	Ferizaj / Uroševac / Ferizaj	MUHOC / MUHOVCE / MUHOF C	PARCELË / PARCELA / parcel	Pronë private Privatna Imovina Privately owned Land /	BREGU PRELEZ / BREGU PRELEZ / BREGU PRELEZ	6391	Bujqësore - Arat - Arë E Klasës 4 / / Poljoprivredno - Njive - Njiva 4 Klase / / Agriculture - Arable - 4th Class Arable Land / /	1 / 8	Bashkë Posedim / SuDrzavina / co-possessor	03.09.2018